



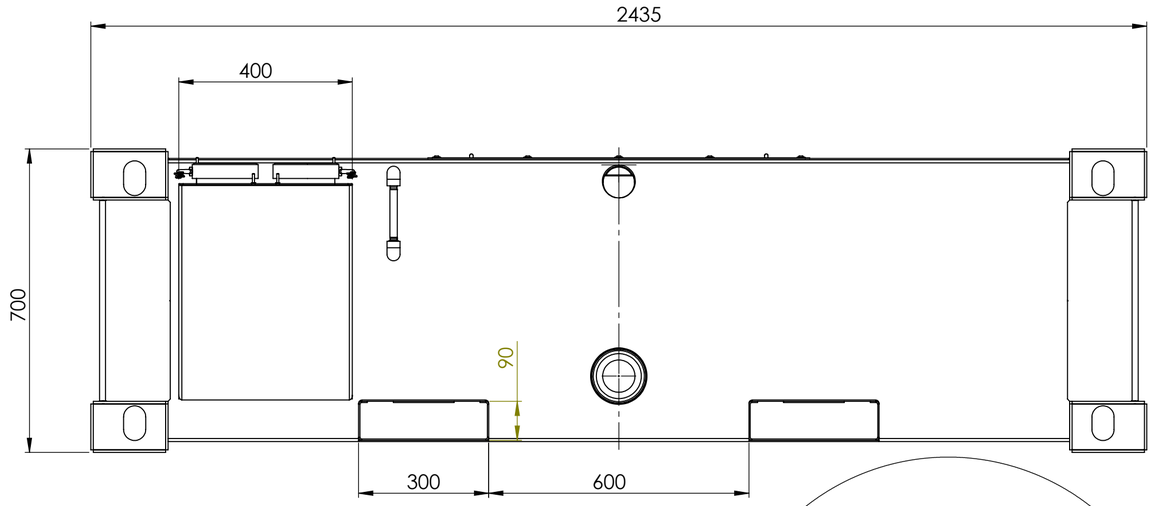


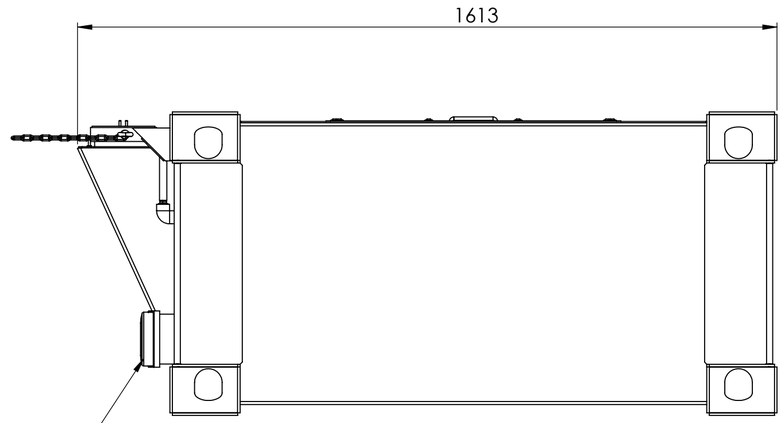

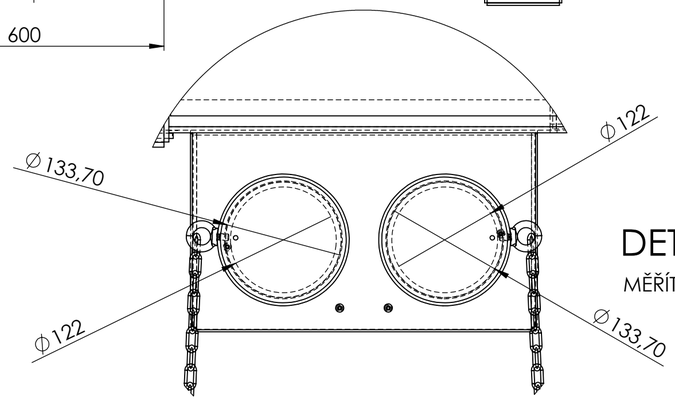

DETAIL A
MĚŘÍTKO 1 : 5

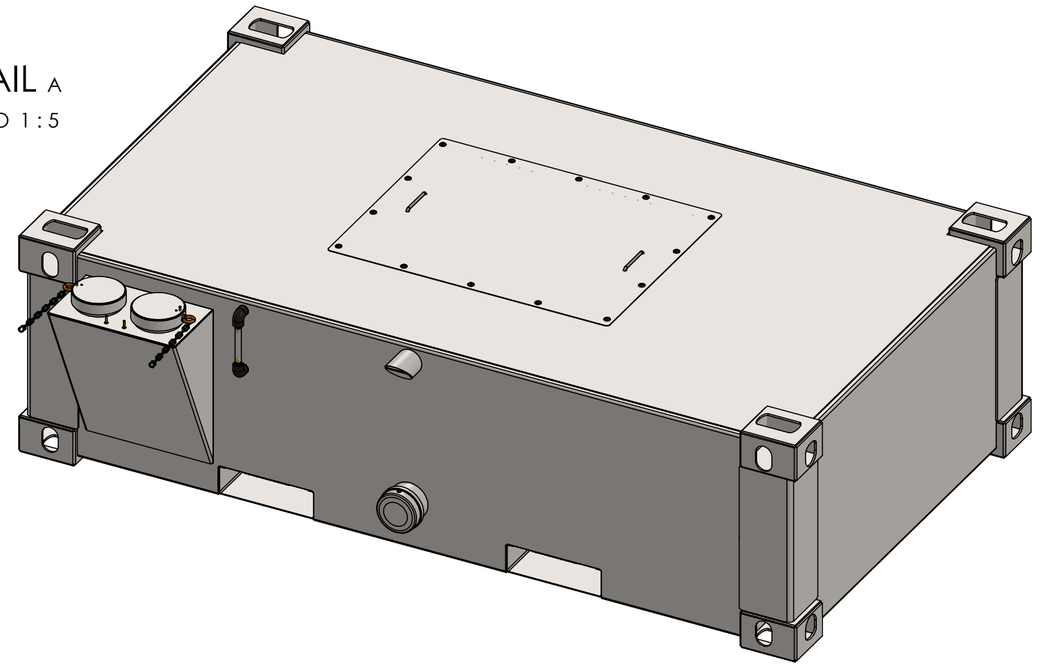

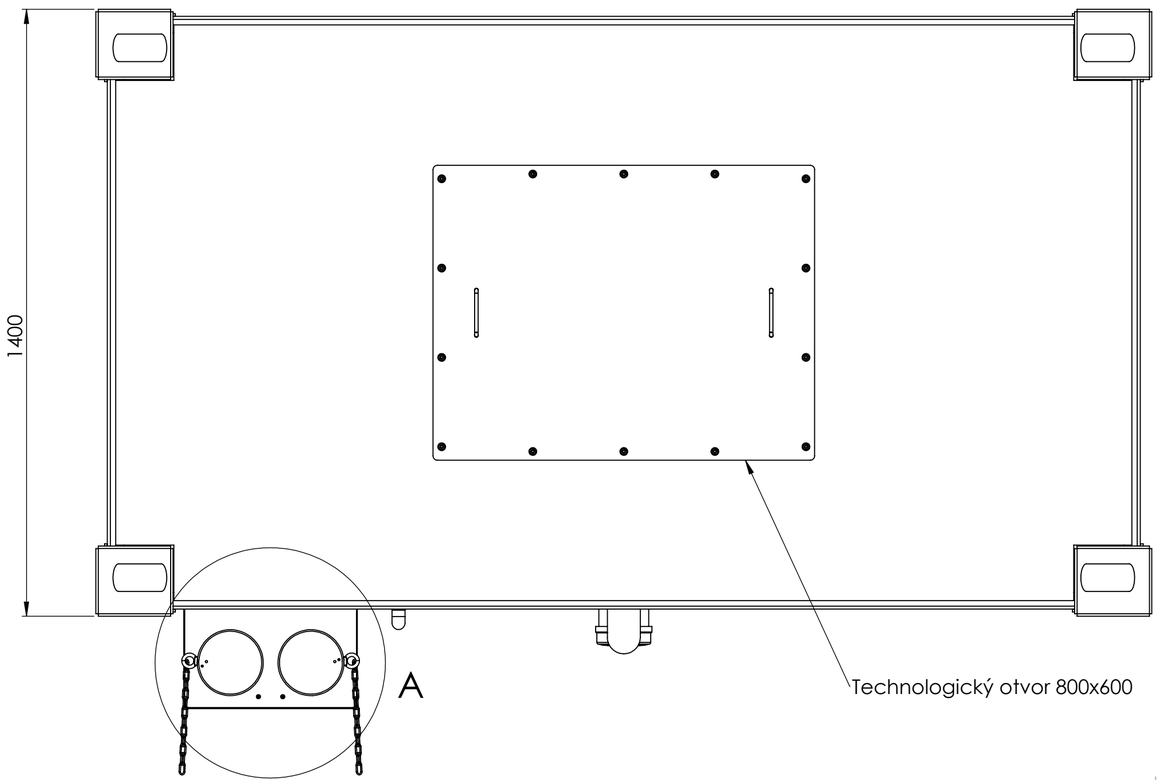

LXS	NÁZOV: **08FT KLASIK**		
	PROJEKT: **08FT KLASIK**		
	POVRCH		
PLEVNÍK-DRIENOVÉ 176 018 26 **PLEVNÍK-DRIENOVÉ**	PRESNOSŤ **ISO 2768 C** TOLERANCIE **ISO 668:2013(E)**		
MIERKA 1:20	HMOTNOSŤ KG 395.95385.41	**DÁTUM** 27. 8. 2026	**FORMÁT** / **LIST**