


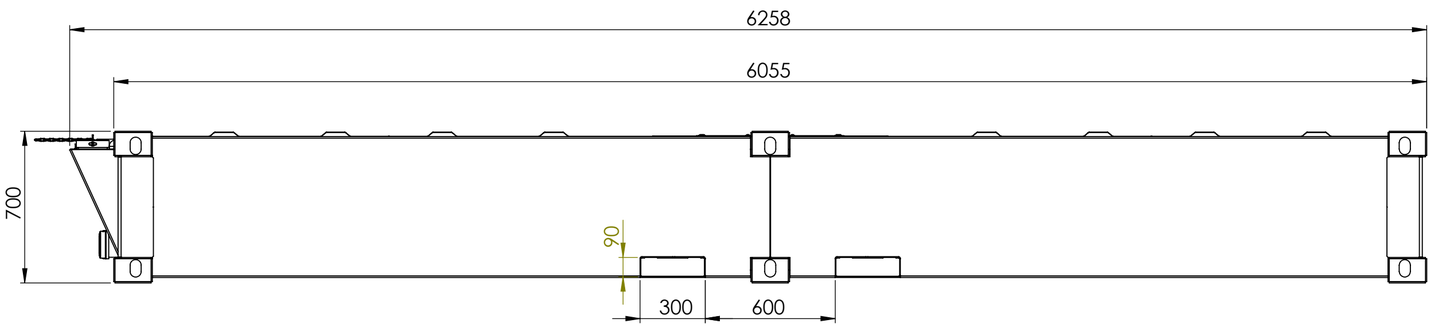


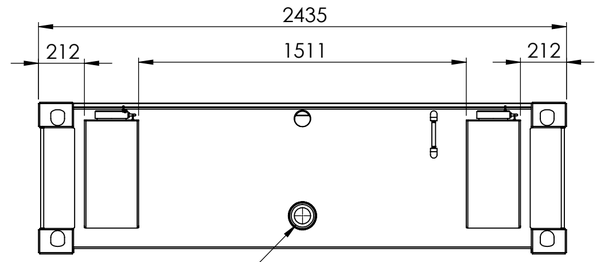


Výpust DN100/4´´

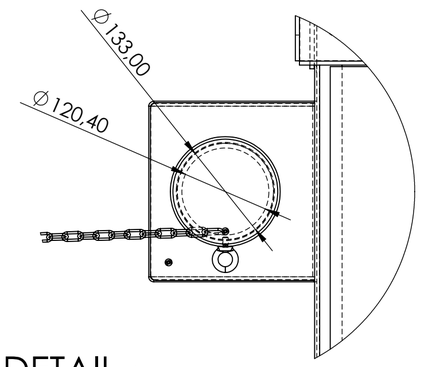


DETAIL A
MĚŘÍTKO 1 : 6

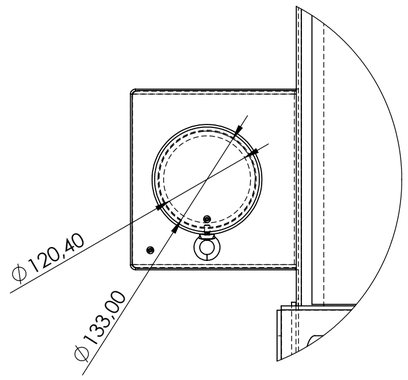

DETAIL B
MĚŘÍTKO 1 : 6

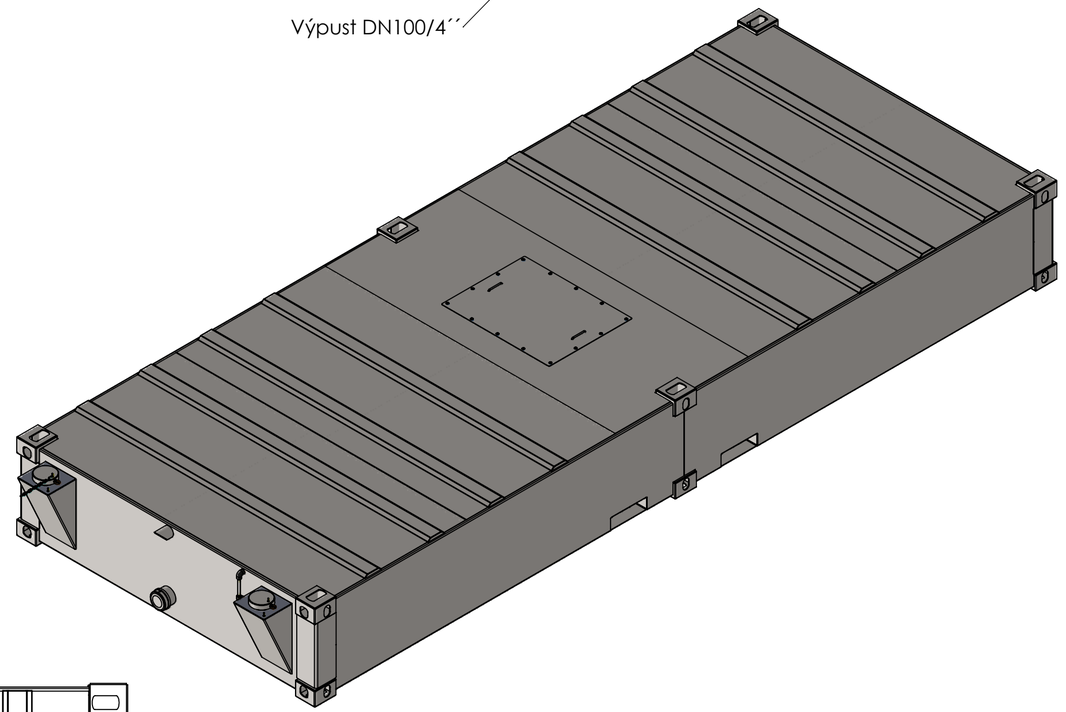

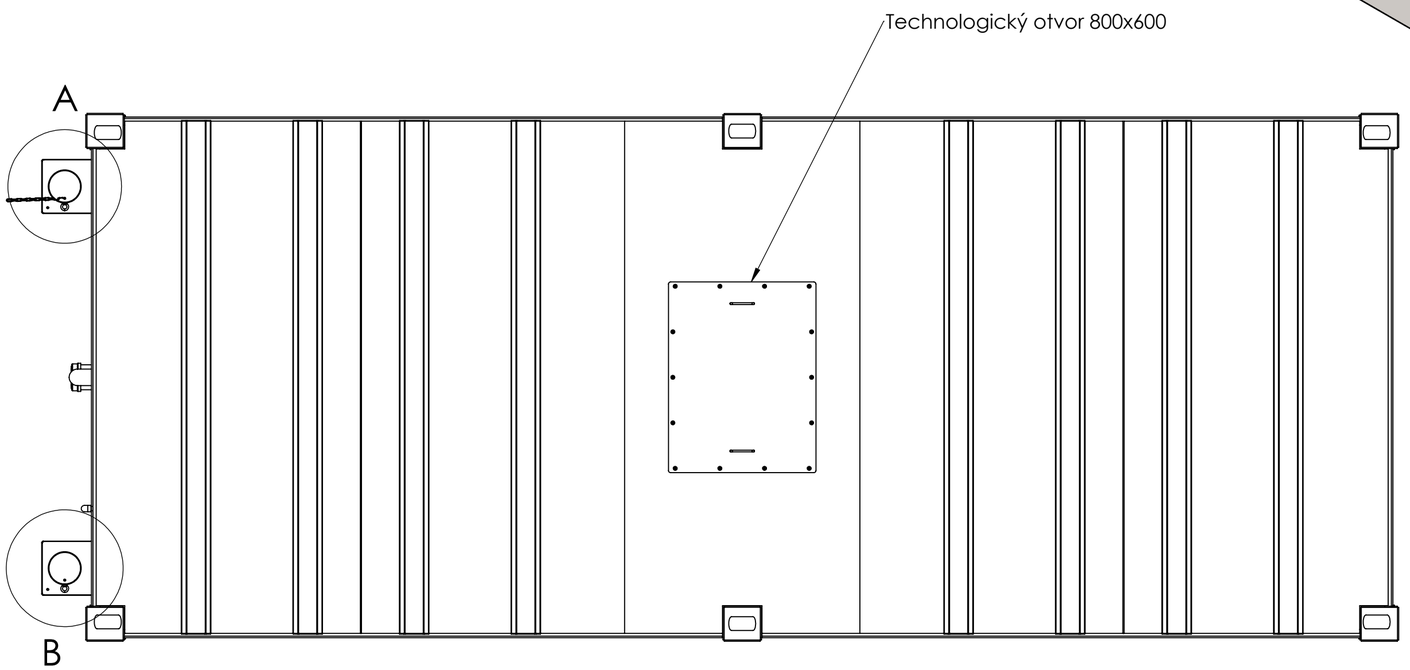

LXS
Plevník-Drienové 176, 018 26, **Plevník-Drienové**

NÁZOV **20FT Klasik**					
PROJEKT **20FT Klasik**					
ČÍSLO ZÁKAZKY					
ČÍSLO VÝROBKU **1102010001**			ČÍSLO KONŠTRUKČNEJ REVÍZIE **RK-08**	ČÍSLO OBJEDNÁVKOVEJ REVÍZIE **RO-04**	DÁTUM 25. 6. 2026
MIERKA **1:50**	HMOTNOSŤ kg **1200**	OBJEM m3 **8**	POVRCH	**ISO 2768 C** **ISO 668:2013(e)** **EN ISO 5817 C**	